


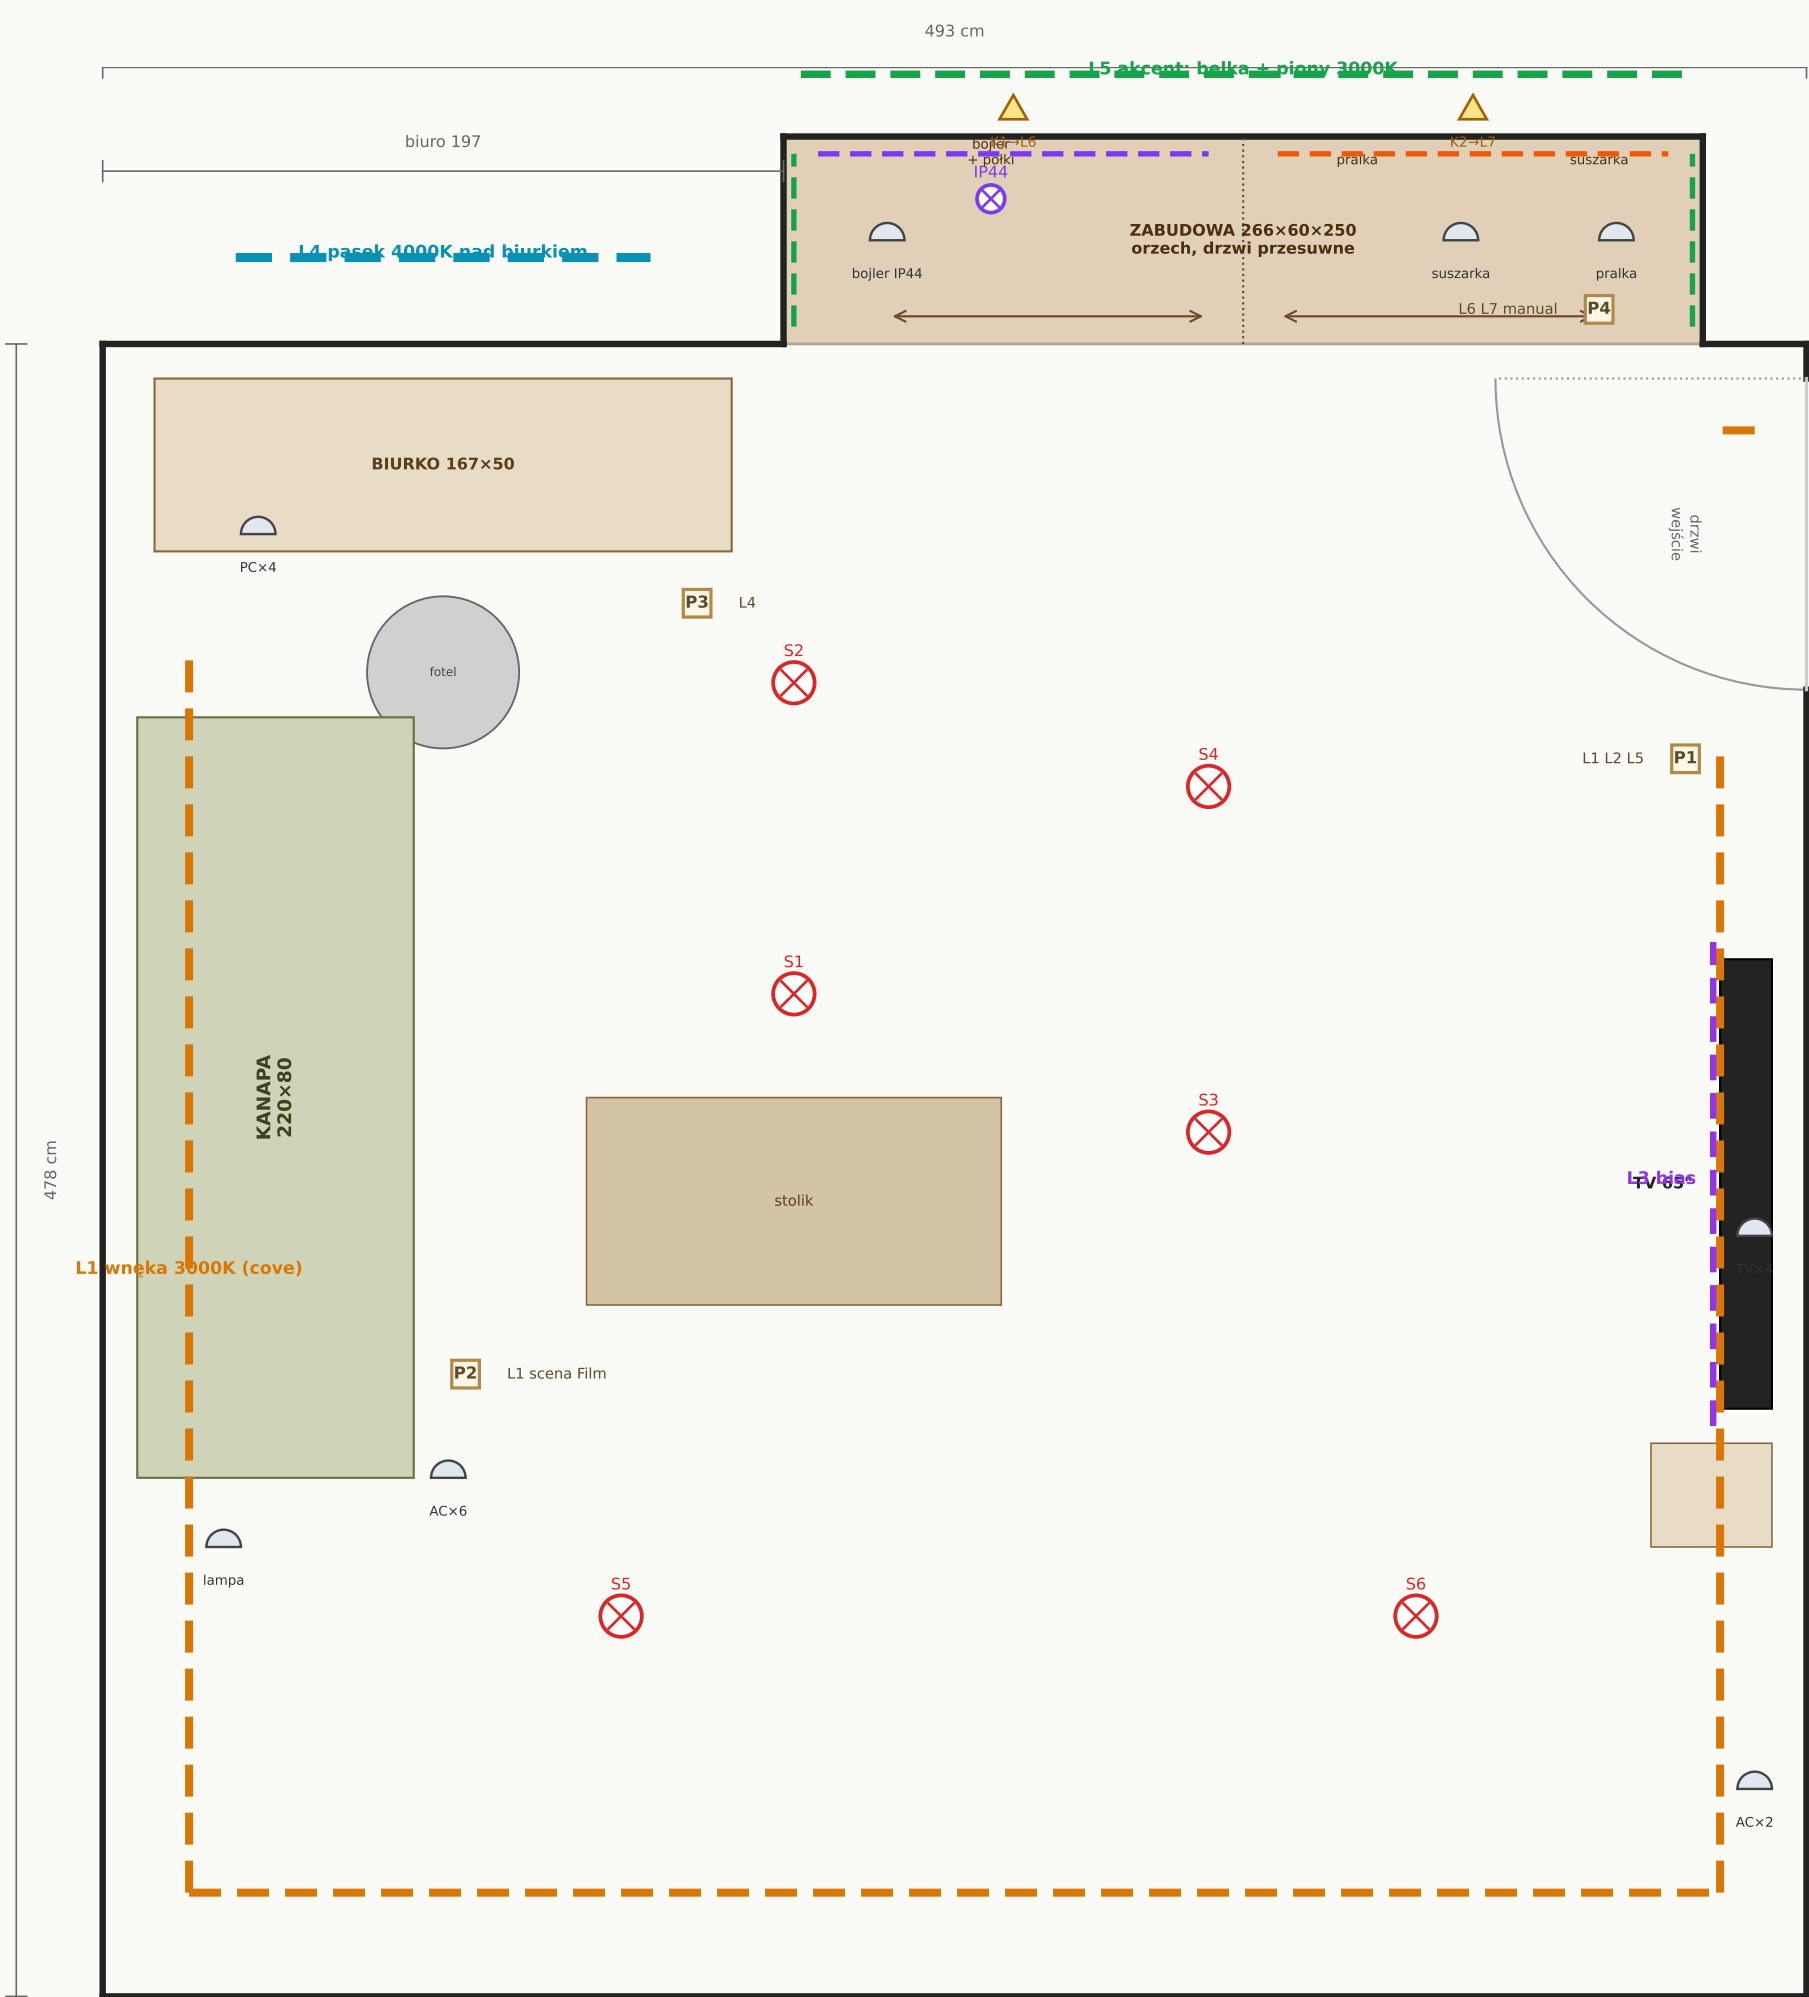

LEGENDA

Obwody (kable w stropie GK):

- L1 — Salon wnęką LED 3000K
- L2 — Salon spoty 3000K
- L3 — Bias TV 3000K
- L4 — Biuro pasek 4000K
- L5 — Zabudowa akcent 3000K
- L6 — Zabudowa wnętrze L 4000K
- L7 — Zabudowa wnętrze P 4000K

Symbole:

- oczeko podtynkowe GU10 (kolor=obwód)
- taśma LED w profilu aluminiowym
- włącznik klawiszowy (Shelly w puszcze), h=110 cm
- kontaktron magnetyczny (w prowadnicy drzwi)
- gniazdo 230V (xN = liczba modułów)

Uwagi:

- wszystkie włączniki na h=110 cm, ta sama seria (np. Berker R.1 / Kontakt-Simon 55 mat)
- każda puszka z przewodem N (neutralnym) — wymaga Shelly
- zasilacze LED 24V w serwerowni / w klapie rewizyjnej GK, NIE w meblu
- L6 i L7 sterowane automatycznie z kontaktronów K1/K2 + P4 awaryjnie
- pralka, suszarka, bojler — każde na osobnym obwodzie B16A + RCD 30 mA