


DETAL 1/2 — PILASTER 15,5 W RZUCIE Z GÓRY (ciąg A, szafki górne)

Pilaster jest PIONOWY — słup na całą wysokość, nie belka pod sufitem. Tu patrzysz na ciąg A od góry.

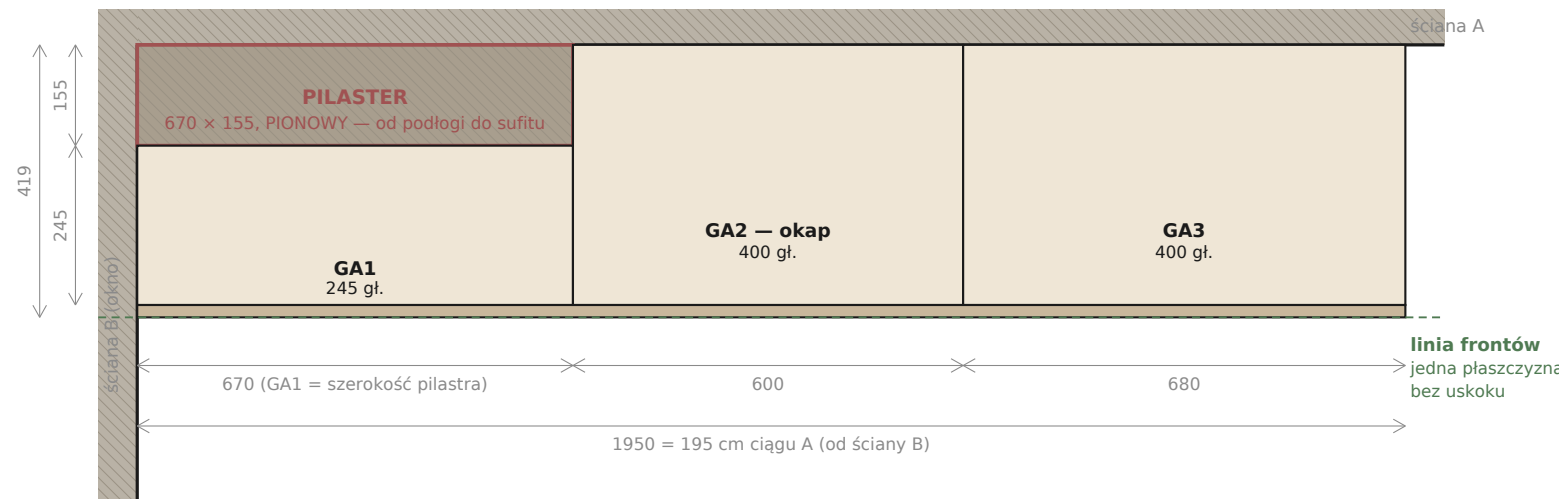

NA TYM POLEGA CAŁA SZTUCZKA

GA1 nie stoi na ścianie — wisi na LICU PILASTRA. Dlatego ma 245 gł., a nie 400: $155 + 245 = 400$.

GA2 i GA3 wiszą na ścianie i mają pełne 400. Efekt: wszystkie fronty w jednej płaszczyźnie, bez uskoku.

I dlatego Twoje 40 cm to dobry wybór: przy standardowych 320 szafka nad pilastrem miałaby $320 - 155 = 165$ mm głębokości — czyli półkę bez sensu. Przy 400 wychodzi 245 mm i szafka realnie działa.

Koszt: fronty stoją 8 cm bliżej głowy (cofnięcie od lica blatu 181 mm zamiast 261 mm).

DETAL 2/2 — KOREKTA PO TWOJEJ UWADZE

Wcześniej odczytałem ten element ze zdjęcia jako belkę pod sufitem. Jest pionowy — poniżej co z tego wynika.

ODWOŁUJĘ (dotyczyło „gzymśu pod sufitem” — nie istnieje)

- wycięcia $160 \times (H_g + 5)$ w bokach szafek GA2, GA3, GC1, GC2 — NIEPOTRZEBNE, nic nie wycinasz
- wieniec górny 240 — wraca normalny, pełne 400
- półka stała wymuszona linią wycięcia — może być zwykła, ruchoma
- listwa montażowa „pod gzymsem” — wraca pod sufit, standardowo
- wycięcia w słupku C2 i nadstawce C4 — niepotrzebne; kratka wentylacyjna wraca na swoje miejsce
- pytanie o wysokość H_g — nieaktualne
- sprzeczność „gzymś vs okno do sufitu” (pkt 11b planu) — nieaktualna, okno spokojnie idzie do sufitu

ZOSTAJE W MOCY (to było policzone dobrze)

- górne szafki 400 gł. — Twoja propozycja; uzasadnienie inne, niż napisałem, ale wniosek ten sam (str. 1)
- GA1 = 245 gł. zamiast 305 — to była realna pomyłka w planie (pilaster wystaje 155, nie 15)
- wszystkie fronty w jednej płaszczyźnie, zabudowa do sufitu 2478
- pilaster 155×670 jest w rzucie od początku — to on odpowiada za różnicę $254,6 - 238,9 \approx 15,5$

JEDNO PYTANIE, KTÓRE MUSZĘ ZADAĆ

Napisałeś, że ten uskok „pomniejsza jakby całe pomieszczenie”. W rzucie mam go jako słup 155×670 przy narożniku ścian A i B — czyli lokalnie, na 67 cm. Ale jeśli te 15,5 idzie wzdłuż CAŁEJ ściany (np. cała ściana A albo cała C), to zmienia się głębokość zabudowy na tej ścianie i trzeba przeliczyć moduły.

Zmierz jedną rzecz: ile centymetrów ma uskok WZDŁUŻ ściany (67 cm czy cała długość?) i przy której ścianie.

KONTROLA Z TWOICH WŁASNYCH WYMIARÓW

$254,6$ (szerokość $A \leftrightarrow C$) — $238,9$ (długość ściany B) = $15,7 \approx 15,5$

To dokładnie ten pilaster. Gdyby uskok szedł wzdłuż całej ściany, ta różnica i tak wyszłaby ta sama — dlatego sam rzut tego nie rozstrzyga i potrzebuję od Ciebie długości uskoku.